



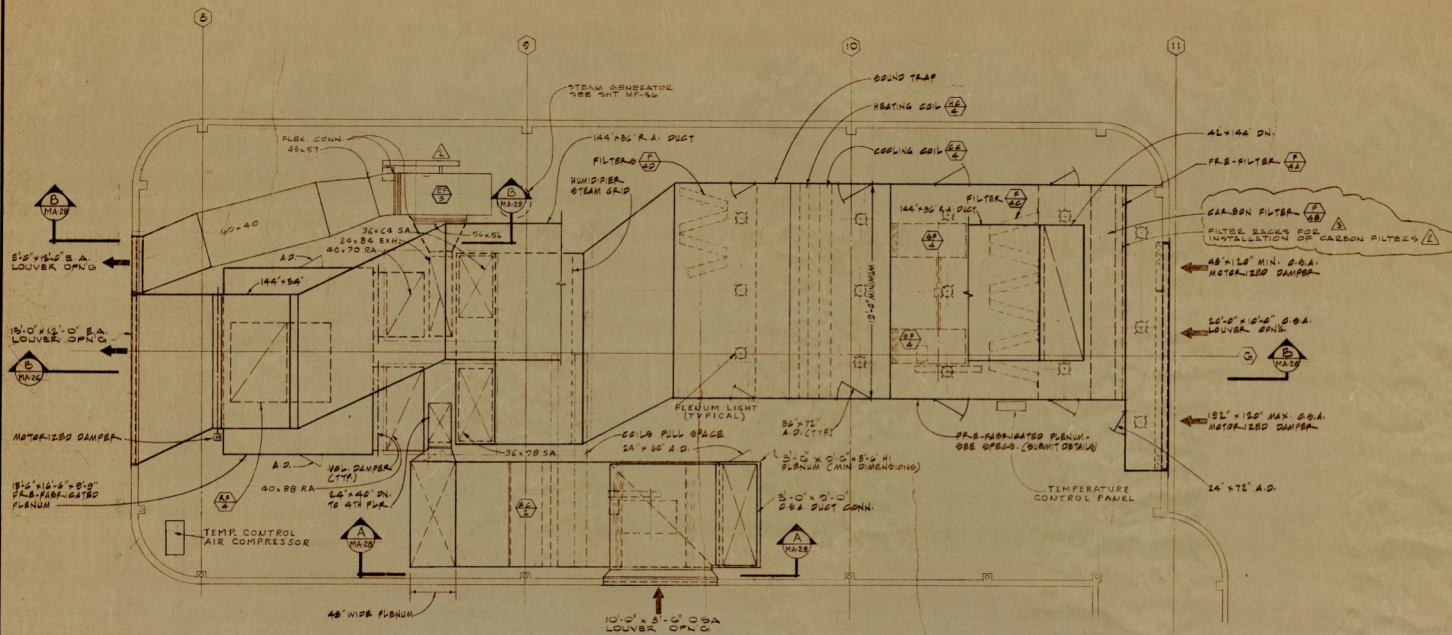


PENTHOUSE MECH. EQUIP. 2ND PLAN - (NORTH WING)  
SCALE: 1/8" = 1'-0"

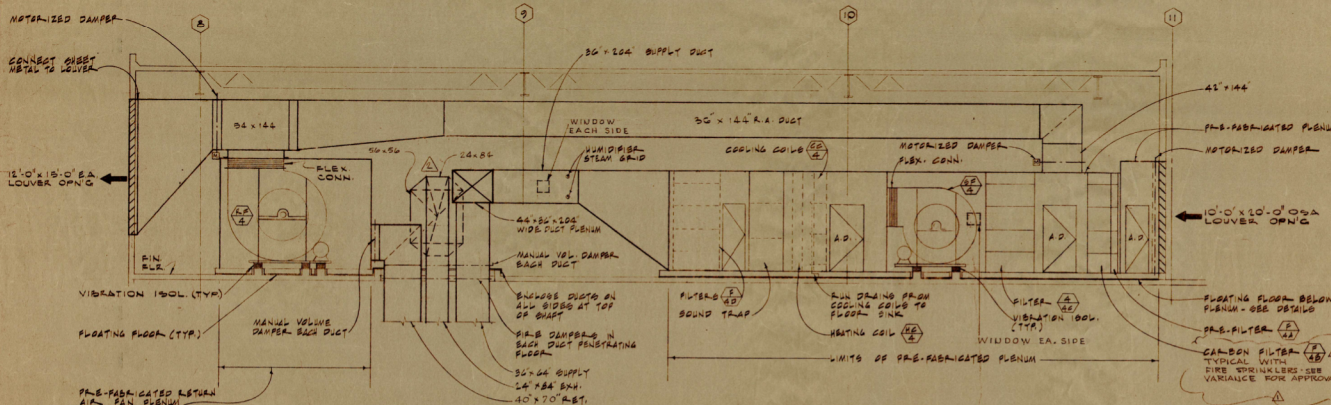

SECTION  
SCALE: 1/8" = 1'-0"

- NOTES:
1. FOR PILING AND PUMP, SEE PLAN (A) 200.
  2. PROVIDE TURNING VANES IN ALL RECTANGULAR DUCT TURN.

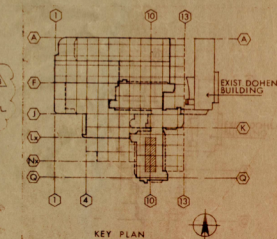

| DATE    | BY                     | REVISION | DATE    | BY                     | REVISION |
|---------|------------------------|----------|---------|------------------------|----------|
| 10/1/78 | INST. MATH. AND EN.    | 10/1/78  | 10/1/78 | INST. MATH. AND EN.    | 10/1/78  |
| 10/1/78 | CONTRACT MODIFICATIONS | 10/1/78  | 10/1/78 | CONTRACT MODIFICATIONS | 10/1/78  |
| 10/1/78 | REVISIONS              | 10/1/78  | 10/1/78 | REVISIONS              | 10/1/78  |
| 10/1/78 | REVISIONS              | 10/1/78  | 10/1/78 | REVISIONS              | 10/1/78  |